THIS MAP IS FOR ASSESSMENT AND TAXATION PURPOSES ONLY

N.E.1/4 S.E.1/4 SEC. 5 T.4N. R.4W. W.M.
COLUMBIA COUNTY

1"= 100'

40405DA

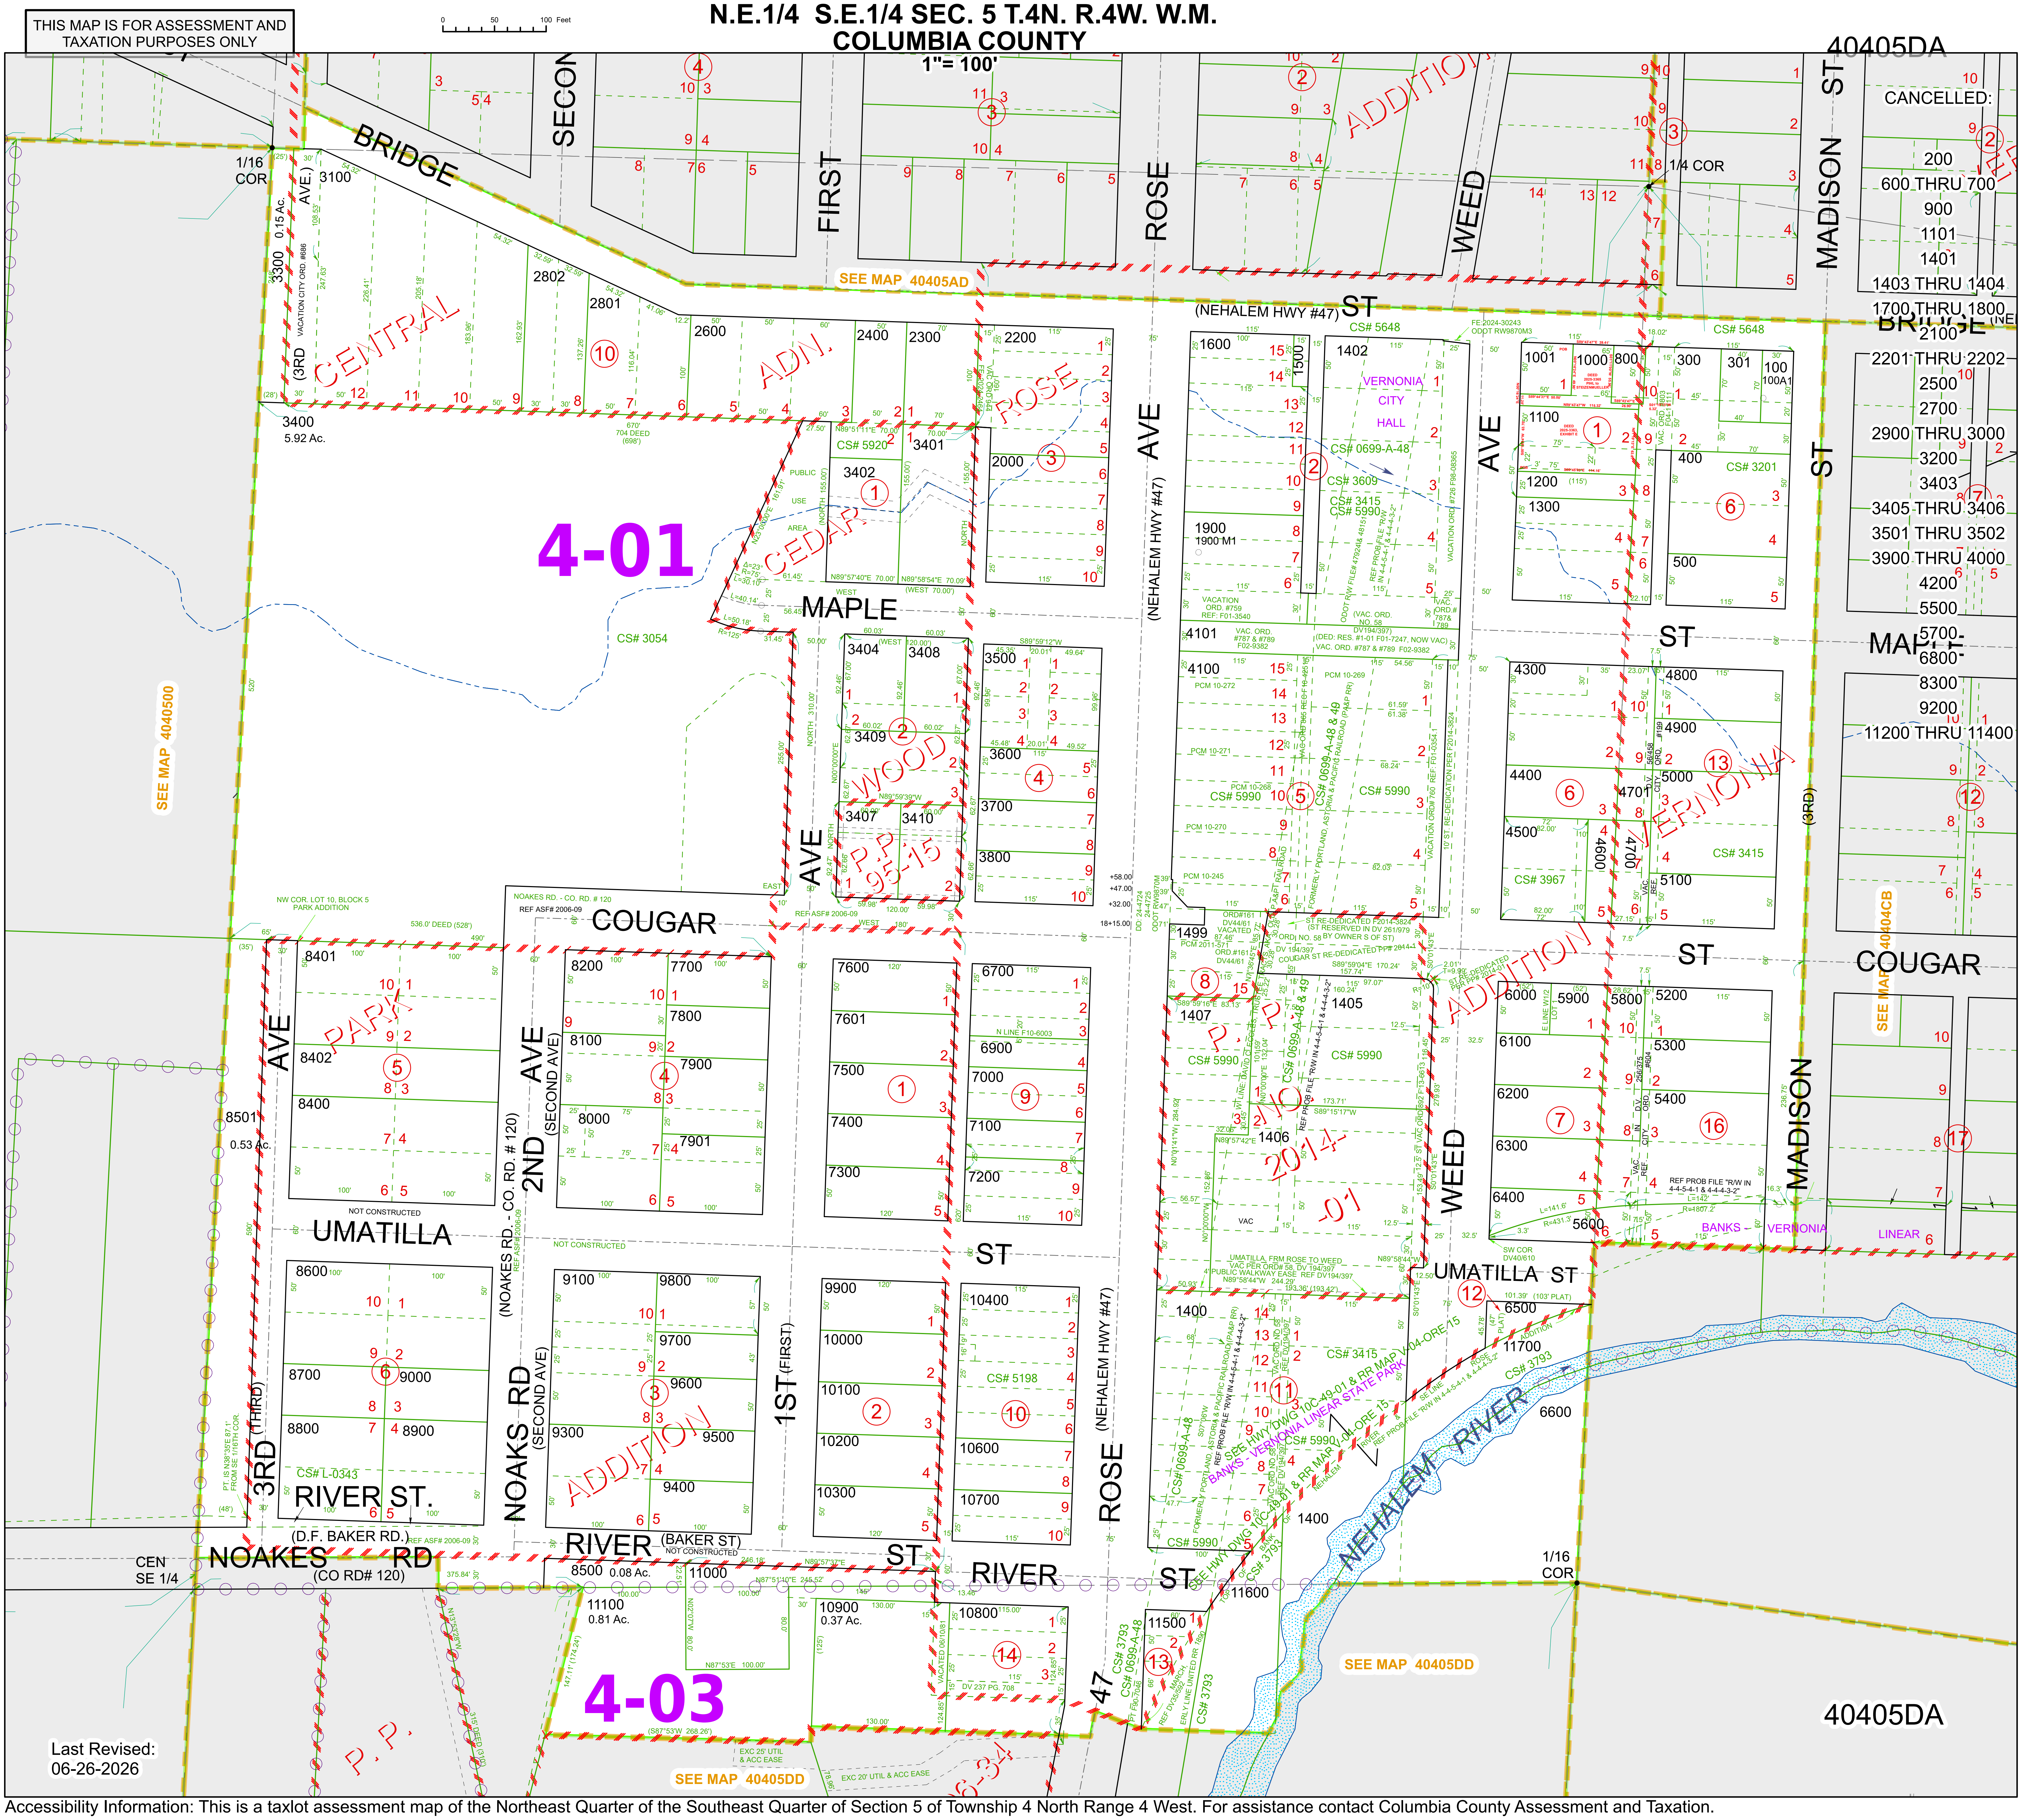
0 50 100 Feet
BRIDGE
SECOND
FIRST
ROSE
WEED
MADISON ST
ST (NEHALEM HWY #47)
SEE MAP 40405AD
SEE MAP 4040500
SEE MAP 40404CB
SEE MAP 40405DD
1/16 COR
1/4 COR
CEN SE 1/4
CANCELLED:
200
600 THRU 700
900
1101
1401
1403 THRU 1404
1700 THRU 1800
2100
2201 THRU 2202
2500
2700
2900 THRU 3000
3200
3403
3405 THRU 3406
3501 THRU 3502
3900 THRU 4000
4200
5500
5700
6800
8300
9200
11200 THRU 11400
4-01
4-03
CENTRAL ADN.
ROSE
CEDAR
WOOD
P.P. 95-15
PARK
ADDITION
VERNONIA ADDITION
P.P. NO. 2014-01
VERNONIA CITY HALL
(3RD AVE.)
VACATION CITY ORD. #686
3100
3300 0.15 Ac.
3400 5.92 Ac.
2802
2801
2600
2400
2300
2200
2000
3402
3401
CS# 5920
CS# 3054
MAPLE ST
3404
3408
3409
3407
3410
3500
3600
3700
3800
AVE
COUGAR ST
1600
1500
1402
1900
1900 M1
4101
4100
1499
1407
1405
1406
1001
1000
800
300
301
100
100A1
1100
1200
1300
400
500
CS# 5648
CS# 0699-A-48
CS# 3609
CS# 3415
CS# 5990
CS# 3201
4300
4800
4900
5000
4400
4701
4500
4600
4700
5100
CS# 3967
8401
8402
8400
8501 0.53 Ac.
8200
7700
7800
8100
7900
8000
7901
7600
7601
7500
7400
7300
6700
6900
7000
7100
7200
6000
5900
5800
5200
6100
5300
6200
5400
6300
6400
5600
UMATILLA ST
NOT CONSTRUCTED
8600
8700
9000
8800
8900
CS# L-0343
RIVER ST.
(D.F. BAKER RD.)
3RD (THIRD)
NOAKS RD (SECOND AVE)
(NOAKES RD. - CO. RD. # 120)
2ND AVE (SECOND AVE)
NOAKES RD (CO RD# 120)
9100
9800
9700
9600
9300
9500
9400
RIVER (BAKER ST) ST
1ST (FIRST)
9900
10000
10100
10200
10300
10400
CS# 5198
10600
10700
(NEHALEM HWY #47)
1400
CS# 3793
6500
11700
6600
12
8500 0.08 Ac.
11000
11100 0.81 Ac.
10900 0.37 Ac.
10800
11500
11600
47
NEHALEM RIVER
BANKS - VERNONIA LINEAR STATE PARK
SEE HWY DWG 10C-49-01 & RR MAP V-04-ORE 15
EXC 25' UTIL & ACC EASE
EXC 20' UTIL & ACC EASE
40405DA

Last Revised:
06-26-2026

Accessibility Information: This is a taxlot assessment map of the Northeast Quarter of the Southeast Quarter of Section 5 of Township 4 North Range 4 West. For assistance contact Columbia County Assessment and Taxation.